



BRIDGE DECK
7350 AB

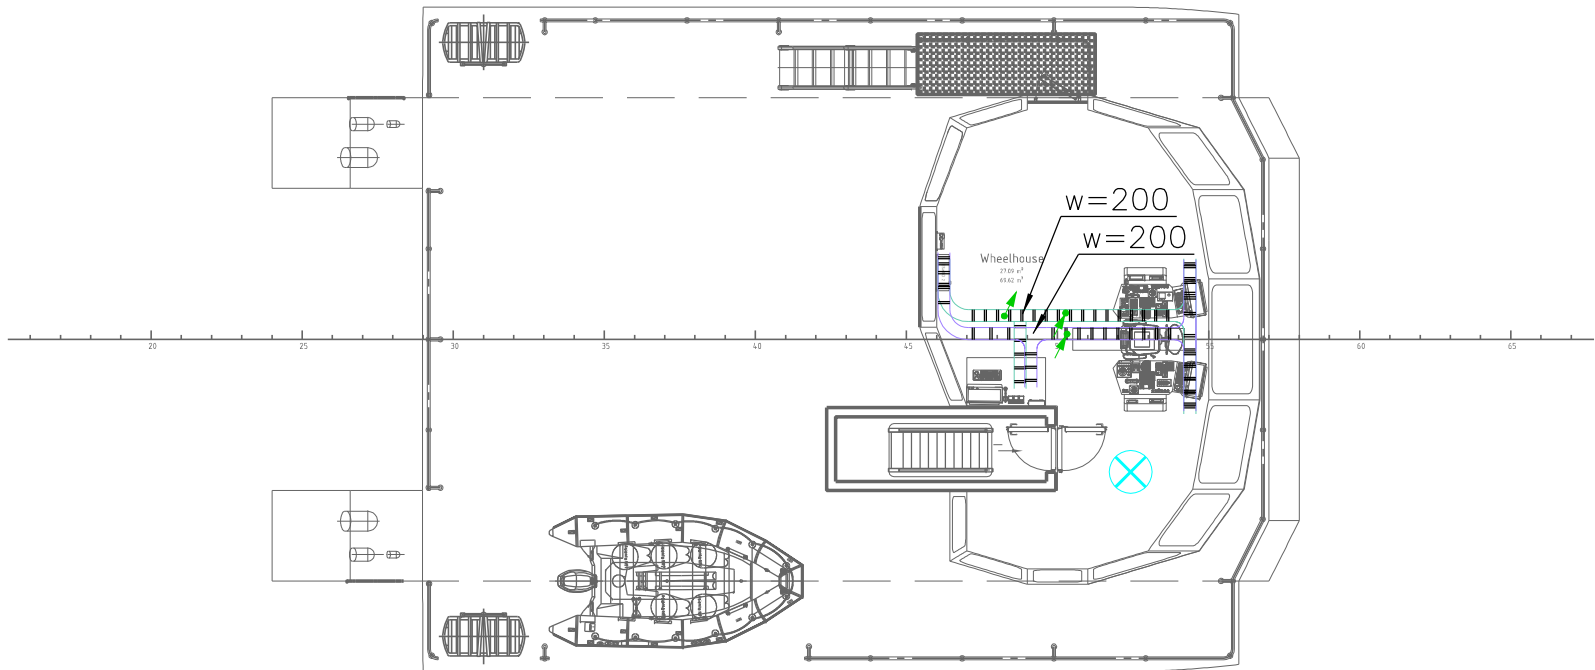

MAIN DECK
4900 AB

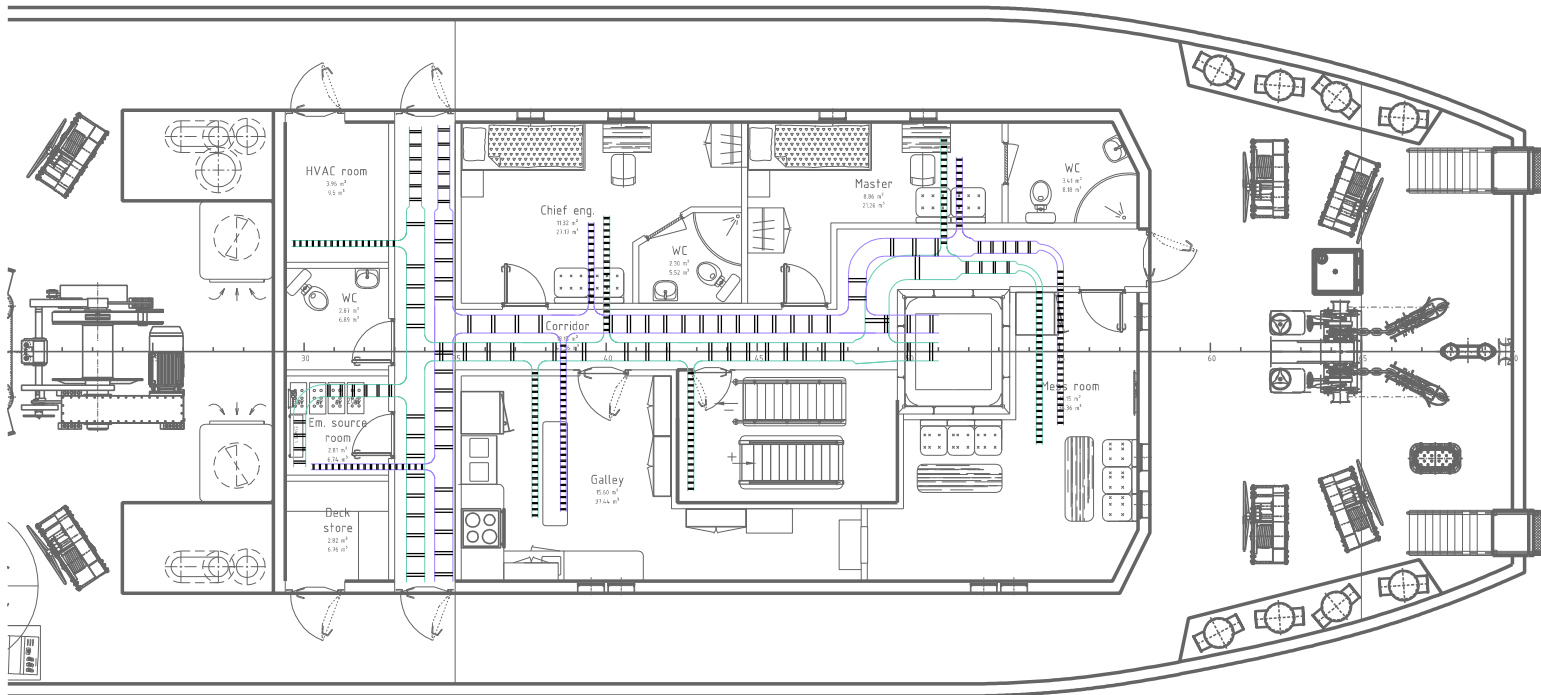

ID	Count	Revision						Init.	Date
District	Area	Site	Reg no.	Authority notes					
				Cable trays					
Hybrid tug				Scale: 1:125					
		Date	27.2.2025	Job no.		Customer no.			
		Draw.	YMU						
		Desig.	YMU						
		Check.	XXX						
		Contact	XXX						
		Sheet							
				Drawing no.		Revision			
				NI22.1112-420-XXX					